

FILE NAME = c:\pwworking\hydot\p0030432\040140571\0350204_cpt_6A_erw.pln-sw1-01.dgn
DATE/TIME = 3/26/2026
USER = p0030432

DESIGN SUPERVISOR K.S. CHAU

JOB MANAGER C. LAMA


DESIGN J.P. O'LOUGHLIN

CHECK X. WANG


DRAFTING J. CAYETANO

CHECK X. WANG

PROJECT MANAGER C. LAMA

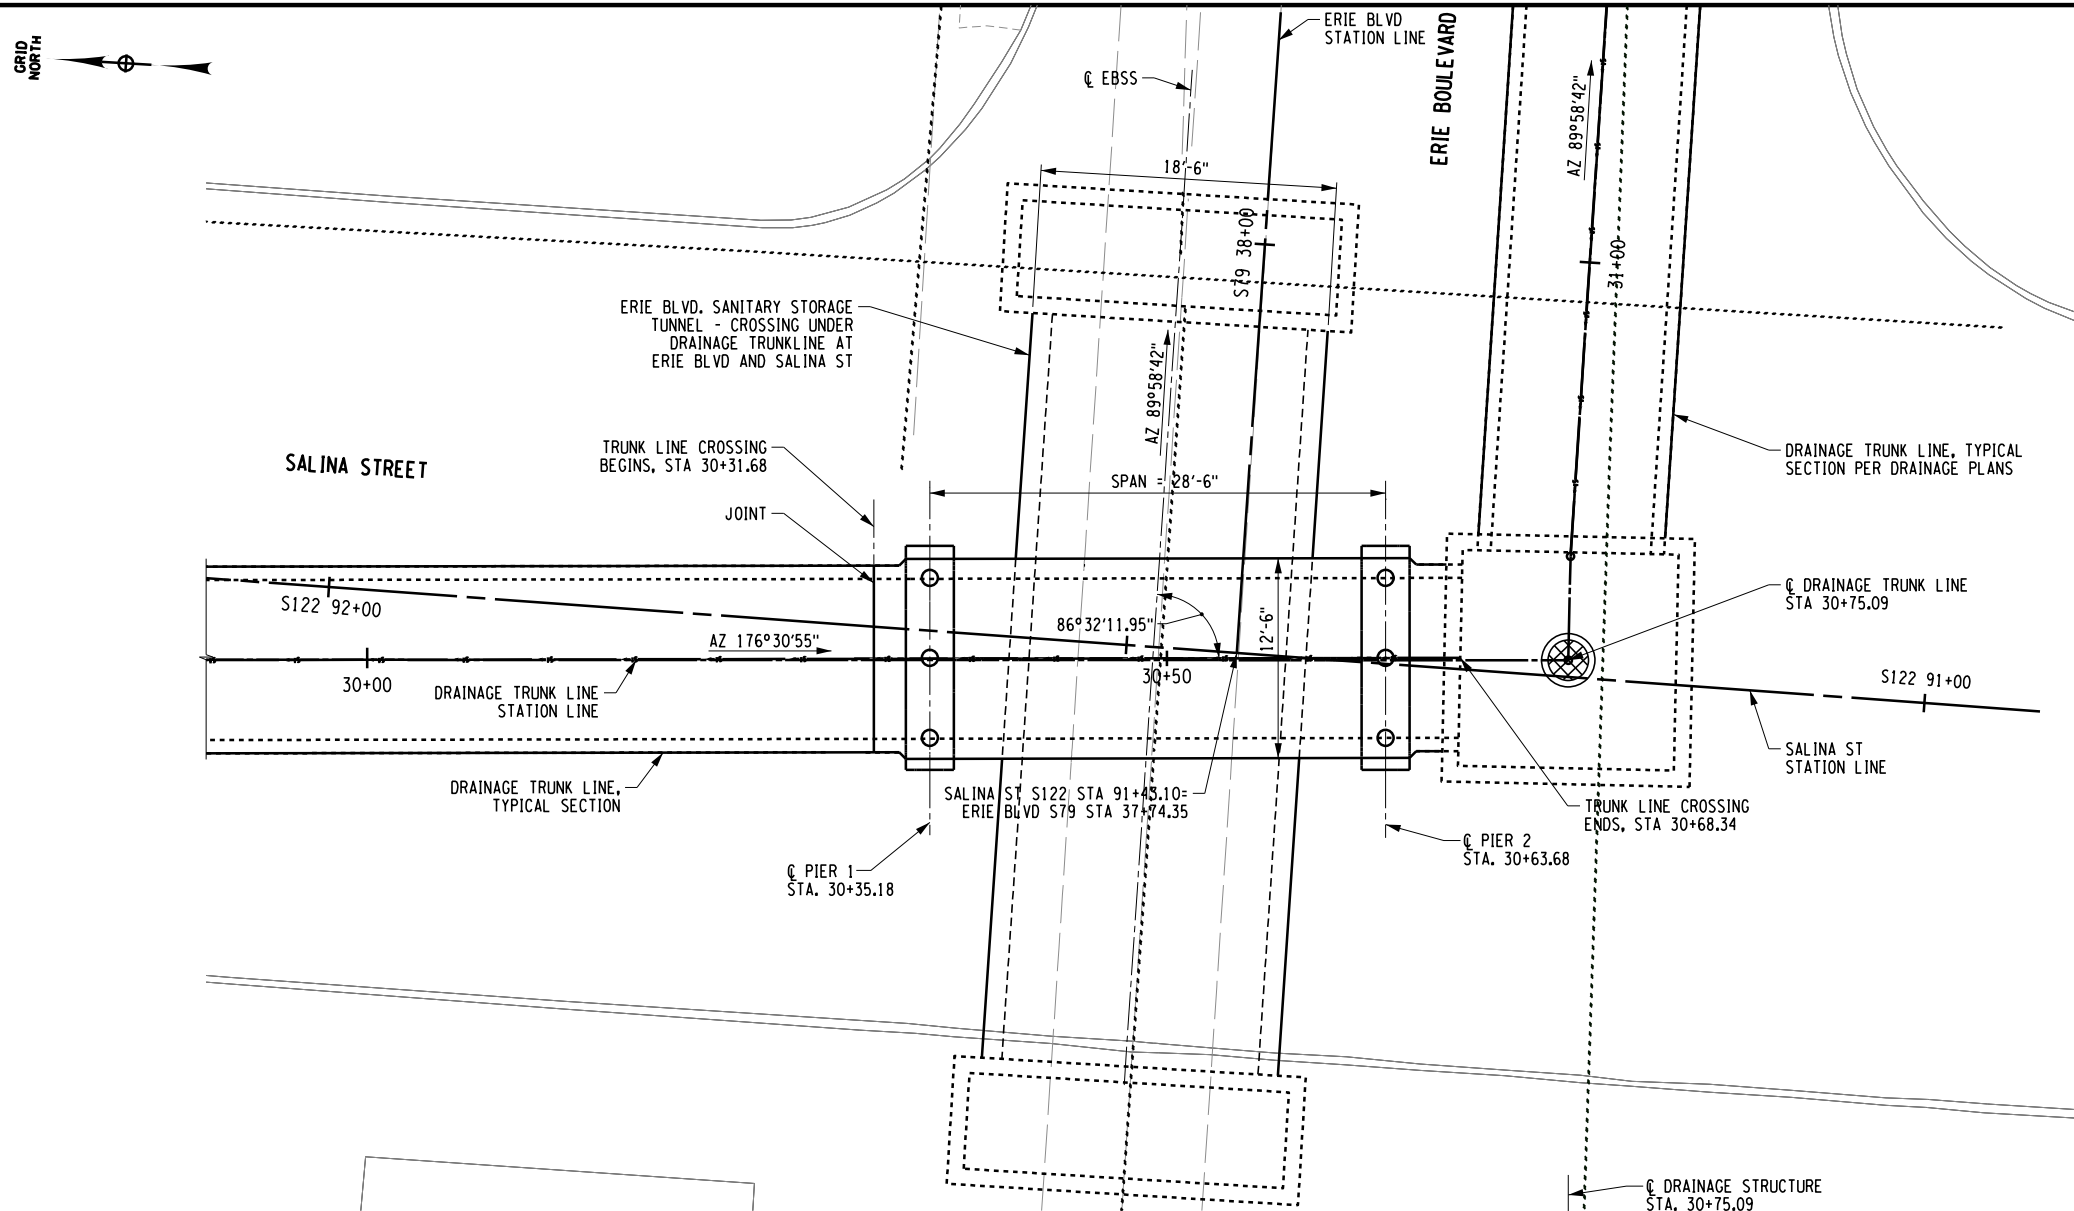


EBSS CROSSING 1 - PLAN VIEW

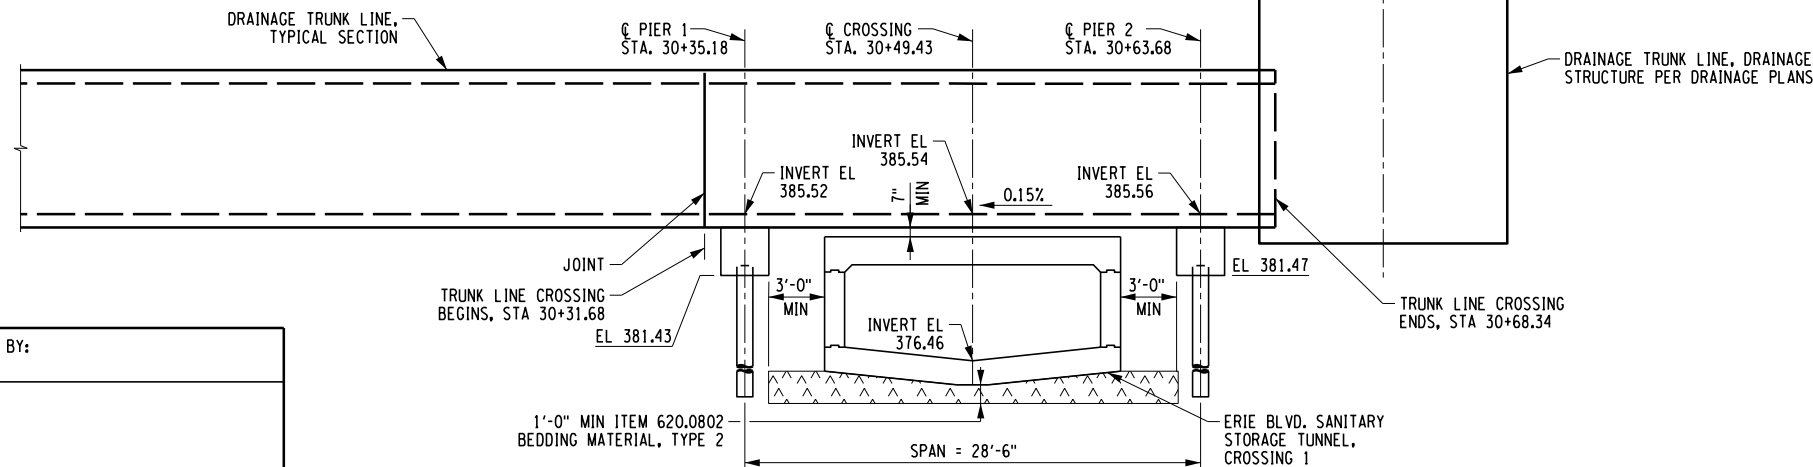

EBSS CROSSING 1 - ELEVATION VIEW

NOTES:

1. DRAINAGE TRUNK LINE CROSSING 1 IS DESIGNED TO SPAN OVER ERIE BLVD SANITARY STORAGE TUNNEL (EBSS), REDUCING LOAD APPLIED FROM TRUNK LINE TO EBSS.
2. FOR DETAILS OF TYPICAL DRAINAGE TRUNK LINE SECTION AND DRAINAGE STRUCTURES, SEE DRAINAGE PLANS.
3. EBSS CROSSING SEQUENCE OF CONSTRUCTION:
 - A. INSTALL SOLDIER PILE AND LAGGING WALL
 - B. INSTALL TEMPORARY ERIE BOULEVARD SANITARY STORAGE TUNNEL (EBSS) TO MAINTAIN FLOW DURING CONSTRUCTION.
 - C. REMOVE EXISTING EBSS.
 - D. INSTALL PROPOSED EBSS AND DRAINAGE STRUCTURES.
 - E. BACKFILL TO BOTTOM OF PROPOSED DRAINAGE TRUNK LINE PIERS.
 - F. INSTALL MICROPILES, PIERS, AND DRAINAGE TRUNK LINE CROSSING.
 - G. CAP DRAINAGE TRUNK LINE ENDS, BRACING AGAINST SOLDIER PILE AND LAGGING WALL.
 - H. BACKFILL TO FINISHED GRADE.

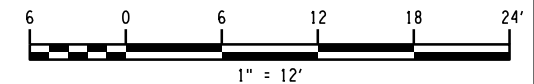

AFFIX SEAL:
ON: 03/26/2026

ALTERED BY:
ON:



AS-BUILT REVISIONS
DESCRIPTION OF ALTERATIONS:

I-81 VIADUCT (COMMUNITY GRID) - CONTRACT 6A
CITY OF SYRACUSE
WATER STREET, SALINA STREET AND HERALD PLACE
COUNTY: ONONDAGA REGION: 3

PIN 3502.04

BRIDGES

CULVERTS

ALL DIMENSIONS IN FT UNLESS OTHERWISE NOTED

CONTRACT NUMBER

TRUNKLINE OVER EBSS - CROSSING 1
GENERAL PLAN AND ELEVATION

D265702

DRAWING NO. SW1-01

SHEET NO. 256

IT IS A VIOLATION OF LAW FOR ANY PERSON, UNLESS THEY ARE ACTING UNDER THE DIRECTION OF A LICENSED PROFESSIONAL ENGINEER, ARCHITECT, LANDSCAPE ARCHITECT, OR LAND SURVEYOR, TO ALTER AN ITEM IN ANY WAY. IF AN ITEM BEARING THE STAMP OF A LICENSED PROFESSIONAL IS ALTERED, THE ALTERING ENGINEER, ARCHITECT, LANDSCAPE ARCHITECT, OR LAND SURVEYOR SHALL STAMP THE DOCUMENT AND INCLUDE THE NOTATION "ALTERED BY" FOLLOWED BY THEIR SIGNATURE, THE DATE OF SUCH ALTERATION, AND A SPECIFIC DESCRIPTION OF THE ALTERATION.

PARSONS



Department of
Transportation

FILE NAME = c:\pwworking\newyork\parsons.p003057\p00140571\0350204_cph.6A_erw_dtl-sw1-07.dgn
DATE/TIME = 3/25/2026
USER = p003057J
DESIGN SUPERVISOR K.S. CHAU

JOB MANAGER C. LAMA


DESIGN J.P. O'LOUGHLIN

CHECK X. WANG


DRAFTING J.P. O'LOUGHLIN

CHECK X. WANG


PROJECT MANAGER C. LAMA

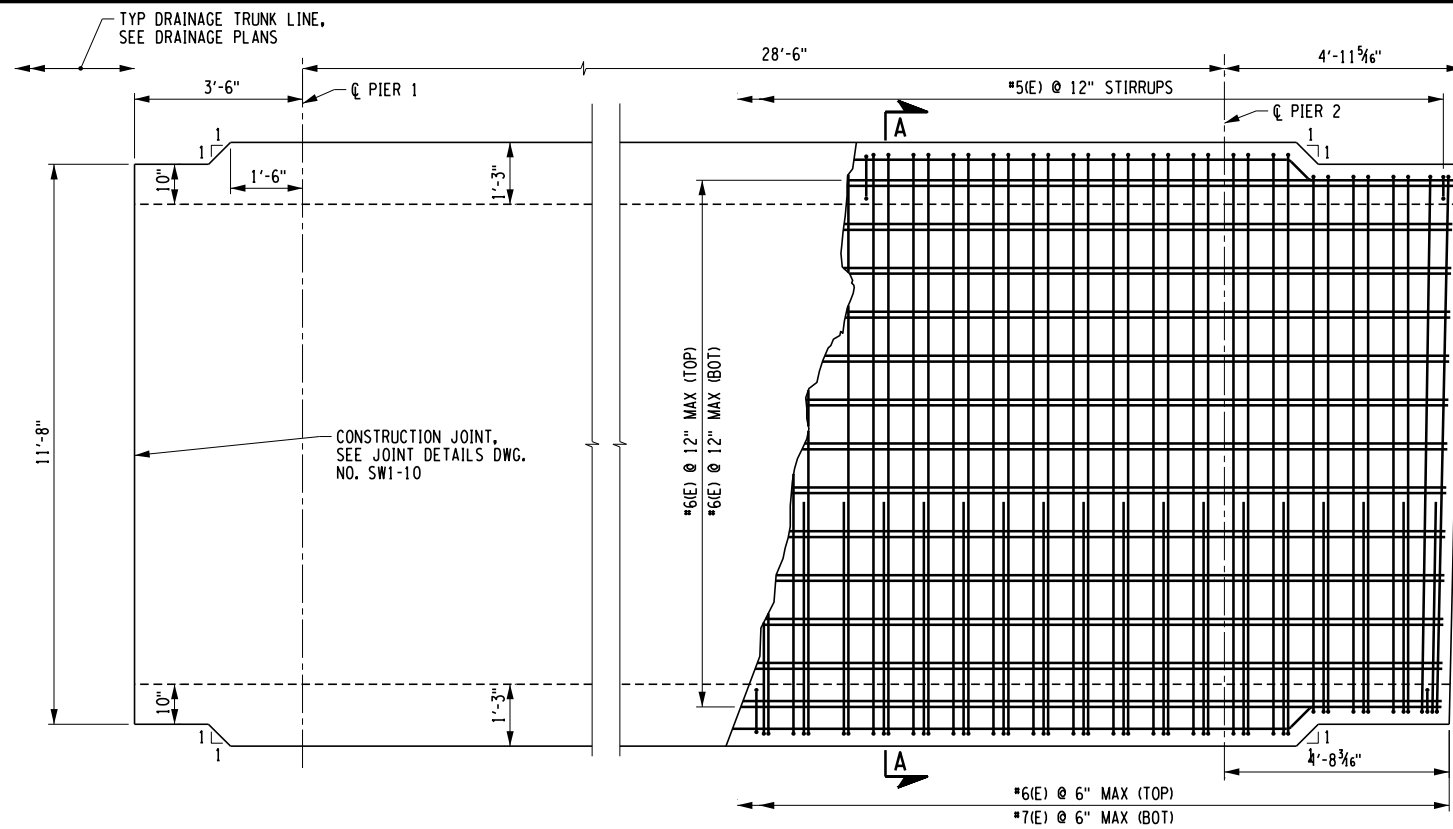


DRAINAGE TRUNK LINE - EBSS CROSSING 1 TOP SLAB PLAN VIEW

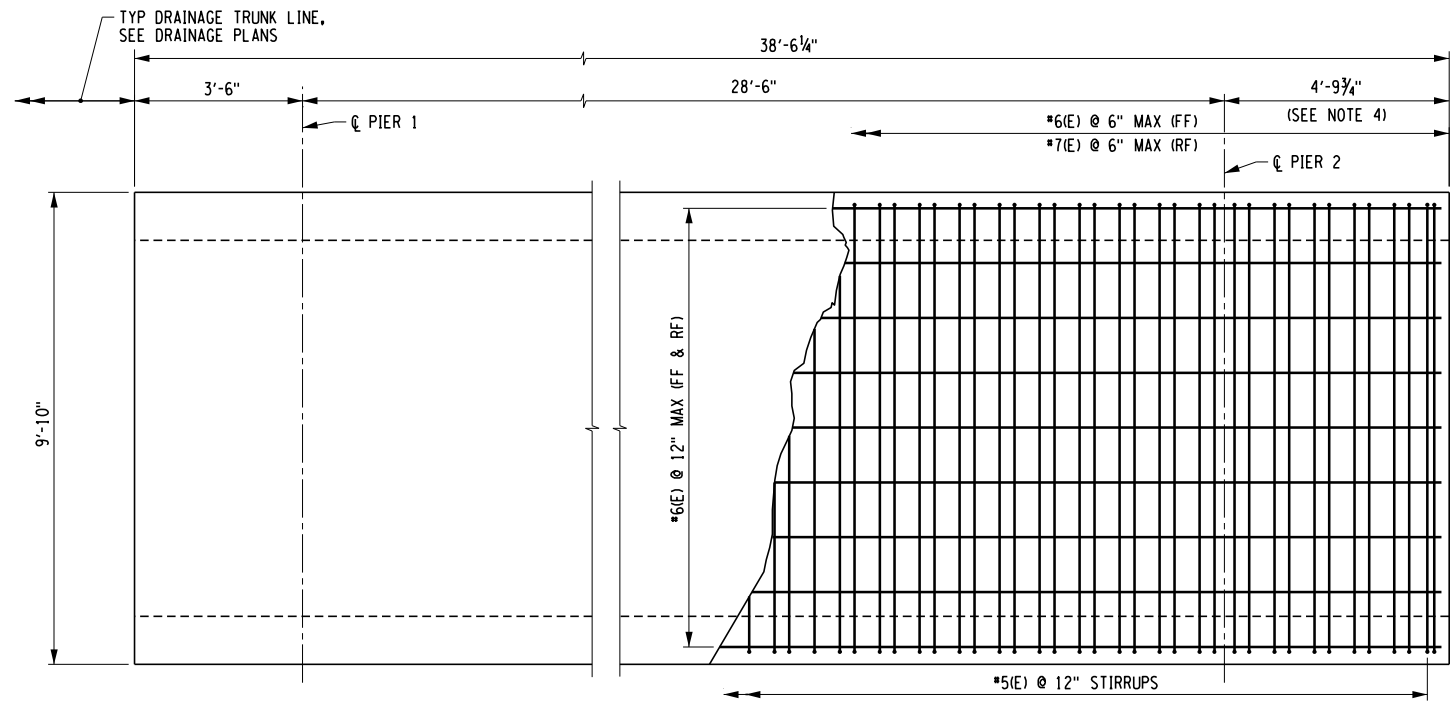

DRAINAGE TRUNK LINE - EBSS CROSSING 1 ELEVATION VIEW

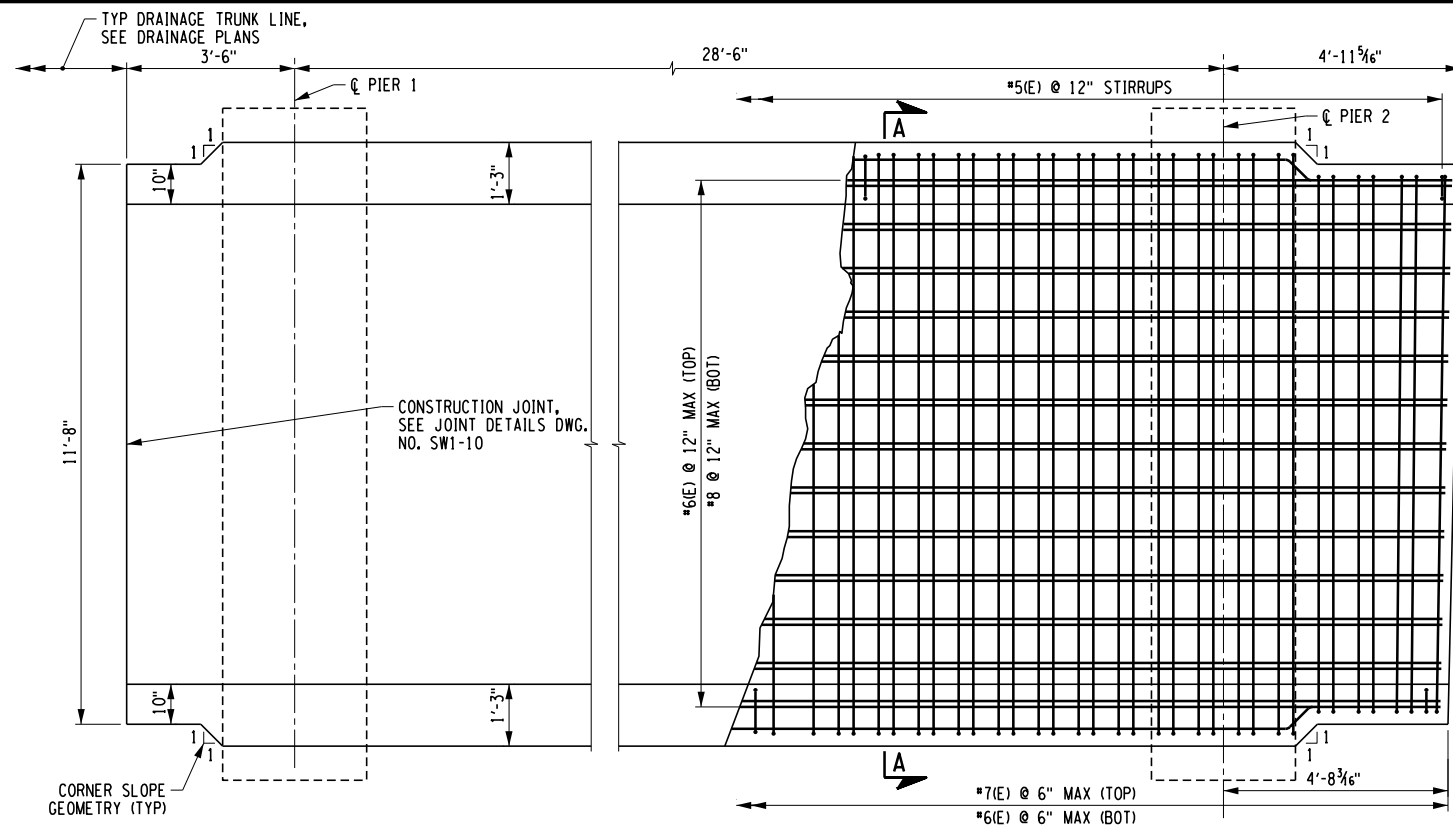

DRAINAGE TRUNK LINE - EBSS CROSSING 1 BOTTOM SLAB PLAN VIEW

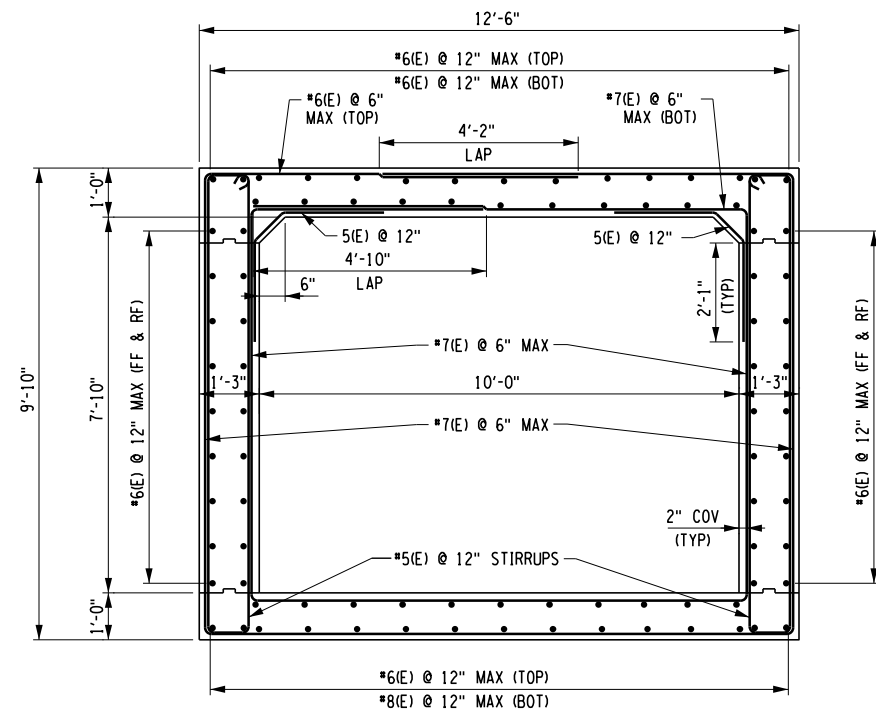


DRAINAGE TRUNK LINE - EBSS CROSSING 1 SECTION A-A

NOTES:

1. ALL REINFORCEMENT PAID FOR UNDER ITEM 556.0202, EPOXY-COATED BAR REINFORCEMENT FOR STRUCTURES.

3. REINFORCEMENT SHOWN FOR CAST IN PLACE CONCRETE. CONTRACTOR MAY ELECT TO INSTALL DRAINAGE TRUNK LINE CROSSING AS CAST-IN-PLACE OR PRECAST CONCRETE. CONTRACTOR SHALL SUBMIT SHOP DRAWINGS INCLUDING REBAR LAYOUT AND BAR LIST TO THE ENGINEER FOR APPROVAL AT LEAST 90 DAYS PRIOR TO INSTALLATION.

4. END DIMENSION IN ELEVATION MEASURED AT CL OF DRAINAGE TRUNK LINE.

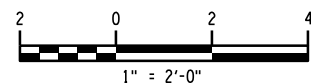

AFFIX SEAL:
ON: 03/26/2026

ALTERED BY:
ON:



AS-BUILT REVISIONS
DESCRIPTION OF ALTERATIONS:

I-81 VIADUCT (COMMUNITY GRID) - CONTRACT 6A
CITY OF SYRACUSE
WATER STREET, SALINA STREET AND HERALD PLACE
COUNTY: ONONDAGA REGION: 3

PIN 3502.04

BRIDGES

CULVERTS

ALL DIMENSIONS IN FT UNLESS OTHERWISE NOTED
TRUNK LINE OVER EBSS - CROSSING 1
REINFORCEMENT DETAILS

CONTRACT NUMBER
D265702
DRAWING NO. SW1-07
SHEET NO. 262

PARSONS



Department of
Transportation

IT IS A VIOLATION OF LAW FOR ANY PERSON, UNLESS THEY ARE ACTING UNDER THE DIRECTION OF A LICENSED PROFESSIONAL ENGINEER, ARCHITECT, LANDSCAPE ARCHITECT, OR LAND SURVEYOR, TO ALTER AN ITEM IN ANY WAY. IF AN ITEM BEARING THE STAMP OF A LICENSED PROFESSIONAL IS ALTERED, THE ALTERING ENGINEER, ARCHITECT, LANDSCAPE ARCHITECT, OR LAND SURVEYOR SHALL STAMP THE DOCUMENT AND INCLUDE THE NOTATION "ALTERED BY" FOLLOWED BY THEIR SIGNATURE, THE DATE OF SUCH ALTERATION, AND A SPECIFIC DESCRIPTION OF THE ALTERATION.

FILE NAME = c:\pwworking\hydot\p0030432\040140571\0350204_cpt_L6A_erw.dgn
DATE/TIME = 3/25/2026
USER = p0030432

DESIGN SUPERVISOR K.S. CHAU

JOB MANAGER C. LAMA


DESIGN J.P. O'LOUGHLIN

CHECK X. WANG


DRAFTING J.P. O'LOUGHLIN

CHECK X. WANG


PROJECT MANAGER C. LAMA

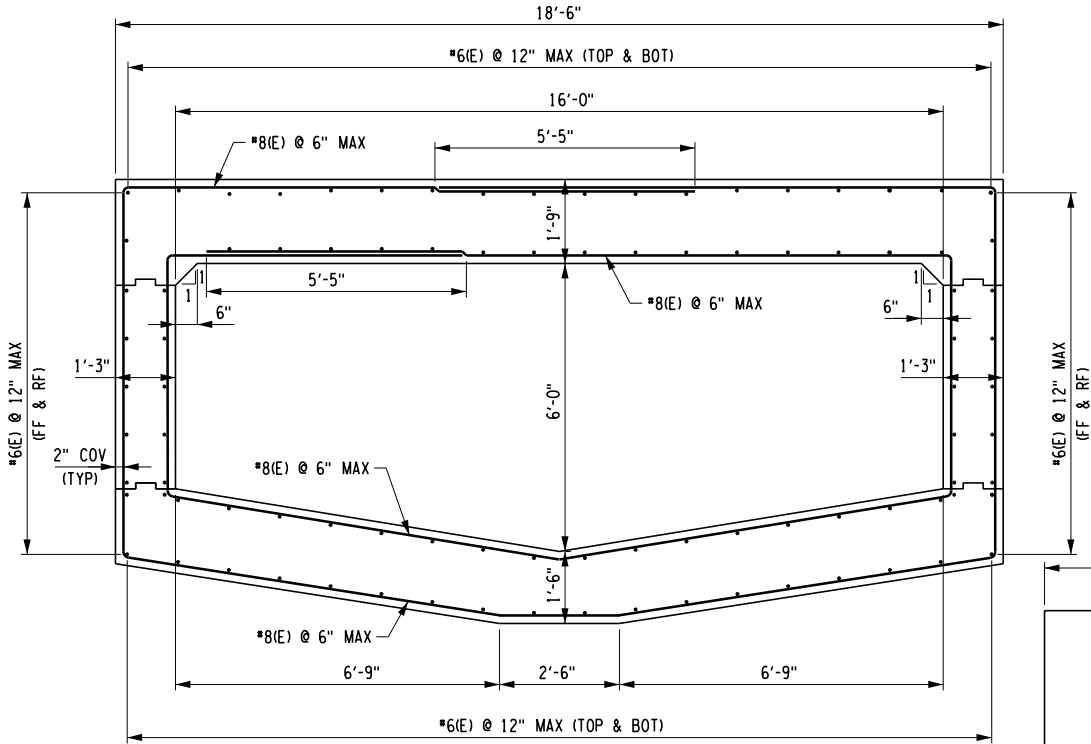


EBSS CROSSING 1 SECTION A - OUTSIDE DRAINAGE TRUNK LINE LIMITS

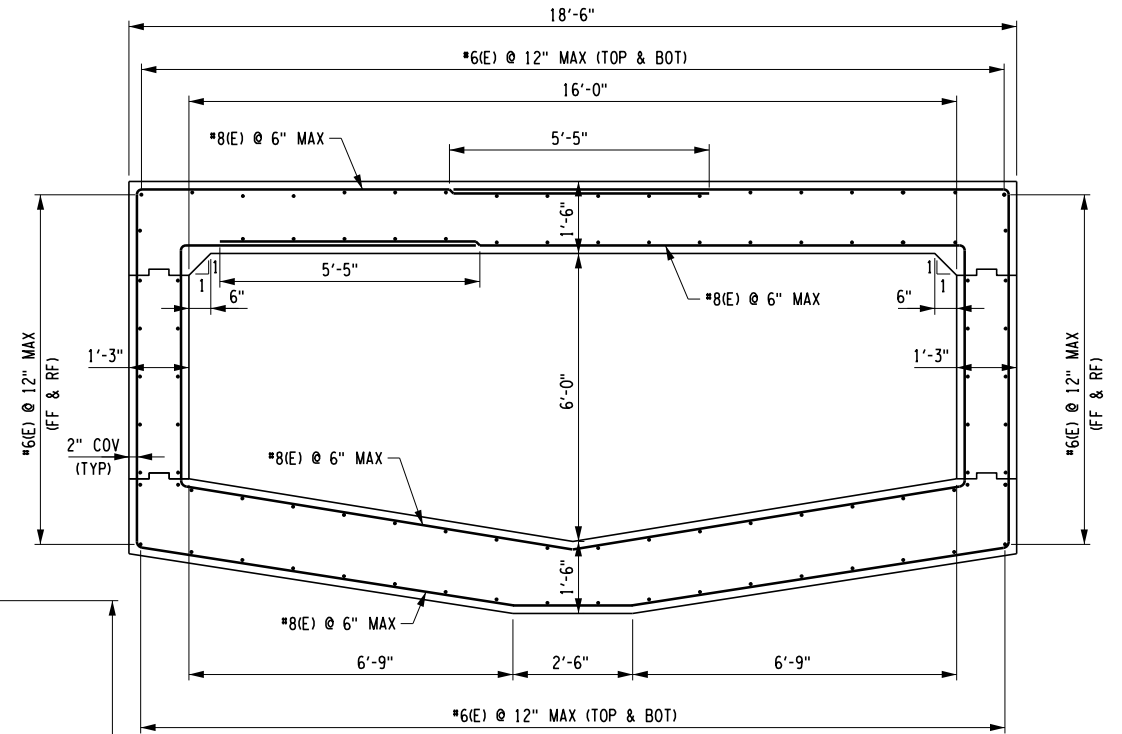

EBSS CROSSING 1 SECTION B - INSIDE DRAINAGE TRUNK LINE LIMITS

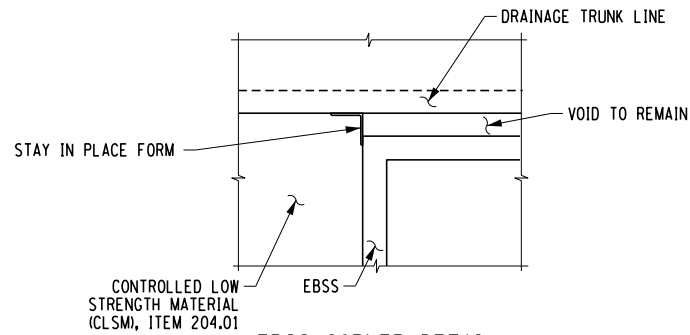


EBSS CORNER DETAIL NTS

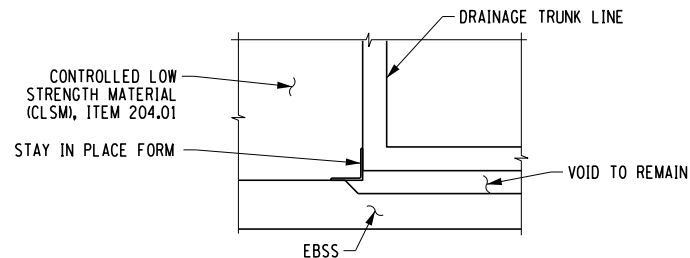


EBSS CORNER DETAIL NTS

NOTE: STAY IN PLACE FORMS SHALL BE PLACED AROUND DRAINAGE TRUNK LINE TO MAINTAIN VOID BETWEEN DRAINAGE TRUNK LINE AND EBSS

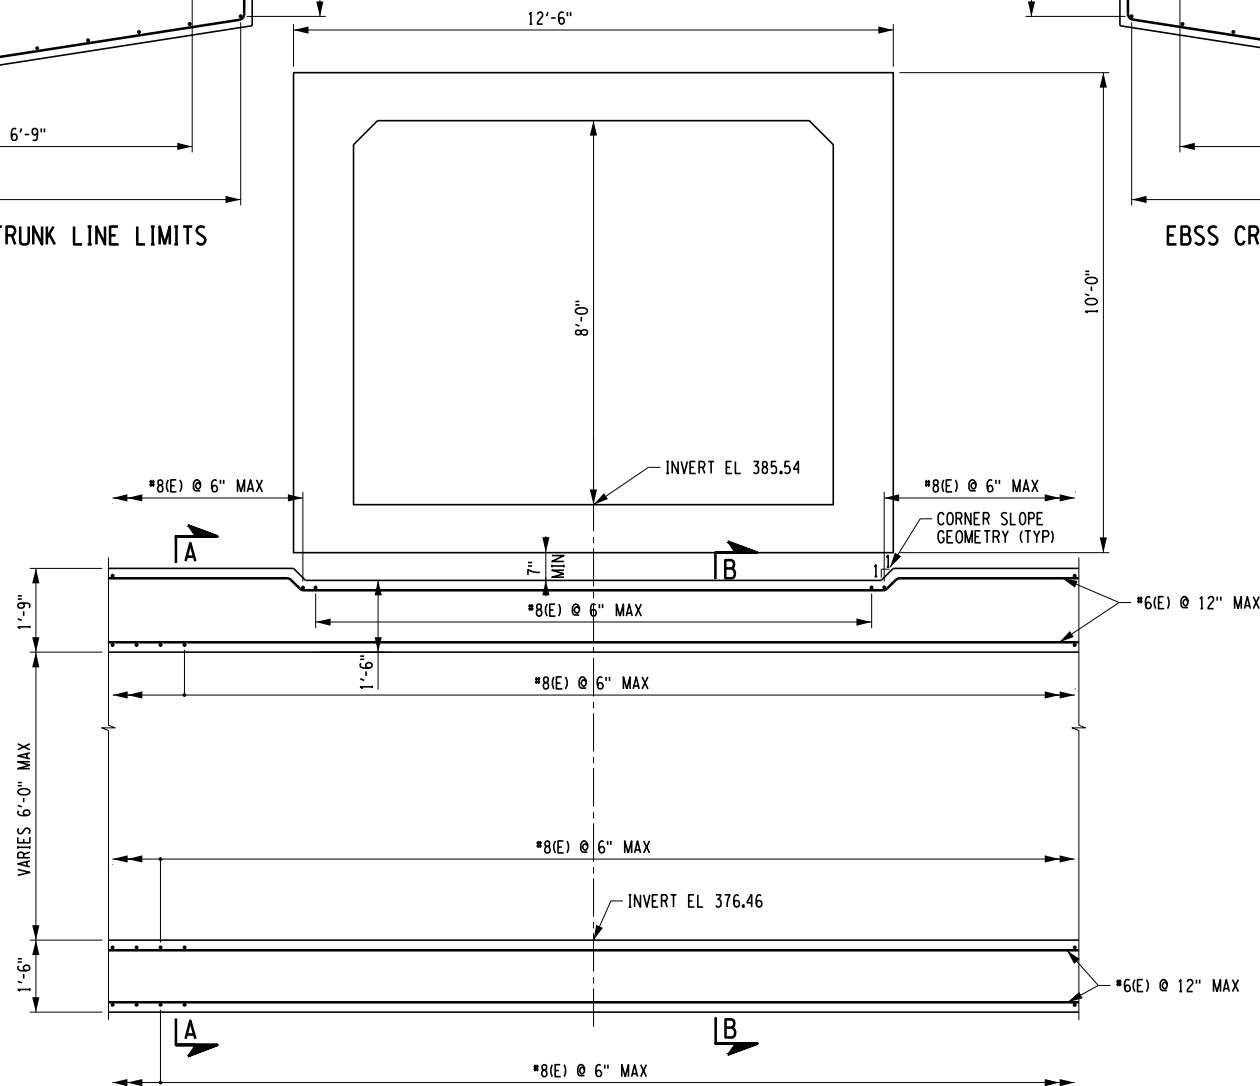

EBSS CROSSING 1 - LONGITUDINAL EBSS SECTION

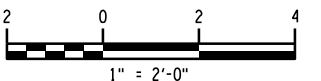

AFFIX SEAL:
ON: 03/26/2026

ALTERED BY:
ON:



AS-BUILT REVISIONS
DESCRIPTION OF ALTERATIONS:

I-81 VIADUCT (COMMUNITY GRID) - CONTRACT 6A
CITY OF SYRACUSE
WATER STREET, SALINA STREET AND HERALD PLACE
COUNTY: ONONDAGA REGION: 3

PIN 3502.04

BRIDGES

CULVERTS

ALL DIMENSIONS IN FT UNLESS OTHERWISE NOTED

CONTRACT NUMBER

D265702

TRUNK LINE OVER EBSS

DETAILS

SHEET 1 OF 4

DRAWING NO. SW1-08

SHEET NO. 263

PARSONS



Department of
Transportation

IT IS A VIOLATION OF LAW FOR ANY PERSON, UNLESS THEY ARE ACTING UNDER THE DIRECTION OF A LICENSED PROFESSIONAL ENGINEER, ARCHITECT, LANDSCAPE ARCHITECT, OR LAND SURVEYOR, TO ALTER AN ITEM IN ANY WAY. IF AN ITEM BEARING THE STAMP OF A LICENSED PROFESSIONAL IS ALTERED, THE ALTERING ENGINEER, ARCHITECT, LANDSCAPE ARCHITECT, OR LAND SURVEYOR SHALL STAMP THE DOCUMENT AND INCLUDE THE NOTATION "ALTERED BY" FOLLOWED BY THEIR SIGNATURE, THE DATE OF SUCH ALTERATION, AND A SPECIFIC DESCRIPTION OF THE ALTERATION.

FILE NAME = c:\pwworking\hydot\p0030432\40140571\0350204_cpt_L6A.erw.dtl-sw1-09.dgn
DATE/TIME = 3/24/2026
USER = p0030432

DESIGN SUPERVISOR K.S. CHAU

JOB MANAGER C. LAMA


DESIGN J.P. O'LOUGHLIN

CHECK X. WANG


DRAFTING J.P. O'LOUGHLIN

CHECK X. WANG


PROJECT MANAGER C. LAMA

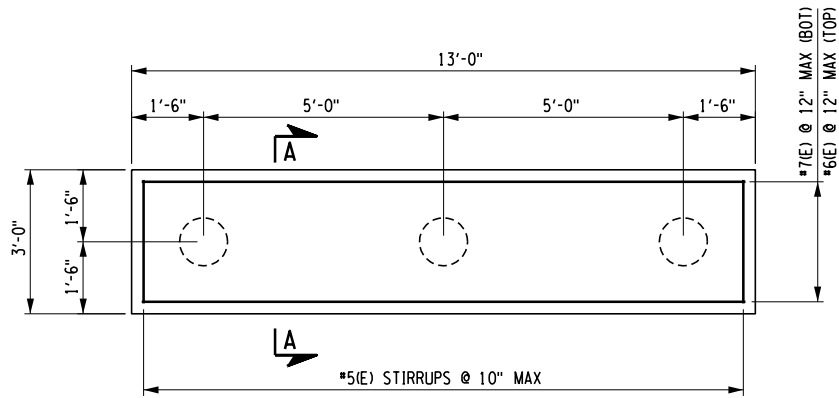


DRAINAGE TRUNK LINE EBSS CROSSING 1 - PILE CAP PLAN

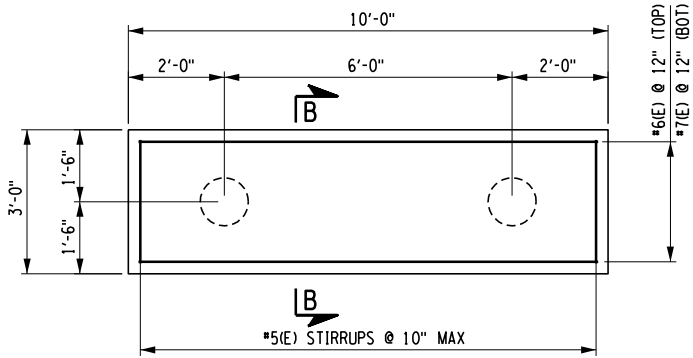


DRAINAGE TRUNK LINE EBSS CROSSING 2 - PILE CAP PLAN

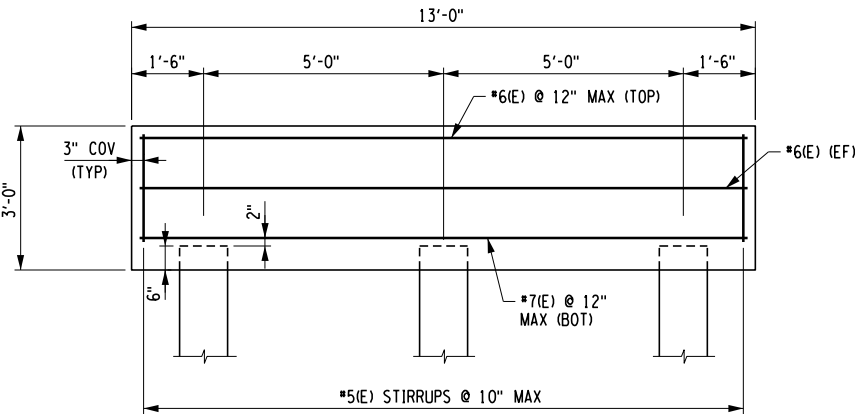


DRAINAGE TRUNK LINE EBSS CROSSING 1 - PILE CAP ELEVATION

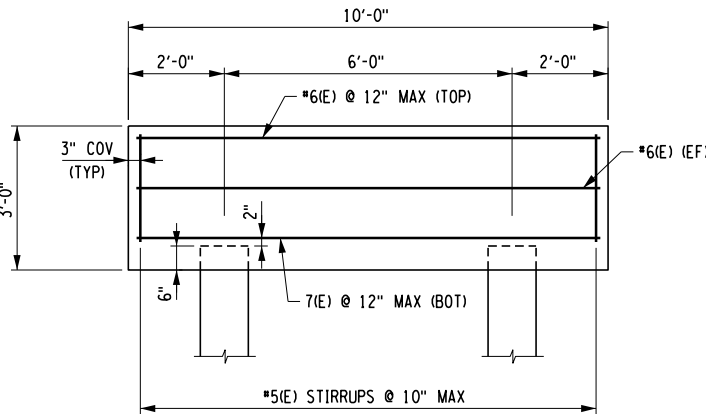

DRAINAGE TRUNK LINE EBSS CROSSING 2 - PILE CAP ELEVATION

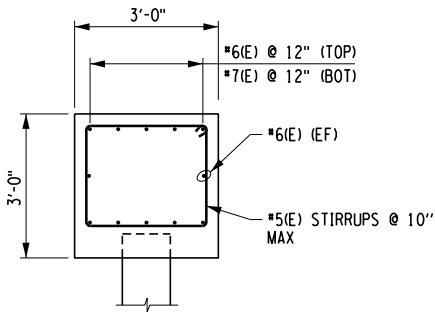

DRAINAGE TRUNK LINE EBSS CROSSING 1 - PILE CAP
SECTION A-A

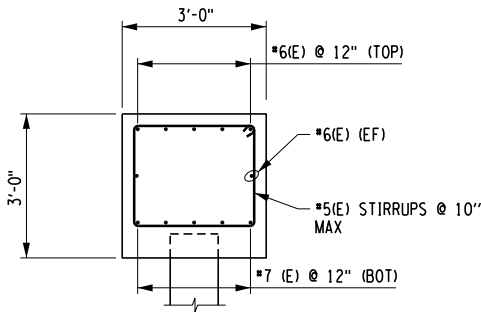

DRAINAGE TRUNK LINE EBSS CROSSING 2 - PILE CAP
SECTION B-B

NOTES:
1. ALL REINFORCEMENT PAID FOR UNDER ITEM 556.0202,
EPOXY-COATED BAR REINFORCEMENT FOR STRUCTURES.

AFFIX SEAL: ON: 03/26/2026	ALTERED BY: ON:

AS-BUILT REVISIONS DESCRIPTION OF ALTERATIONS:	I-81 VIADUCT (COMMUNITY GRID) - CONTRACT 6A	PIN 3502.04		BRIDGES	CULVERTS	ALL DIMENSIONS IN FT UNLESS OTHERWISE NOTED	CONTRACT NUMBER			
	CITY OF SYRACUSE						D265702			
	WATER STREET, SALINA STREET AND HERALD PLACE									
	COUNTY: ONONDAGA						REGION: 3			
IT IS A VIOLATION OF LAW FOR ANY PERSON, UNLESS THEY ARE ACTING UNDER THE DIRECTION OF A LICENSED PROFESSIONAL ENGINEER, ARCHITECT, LANDSCAPE ARCHITECT, OR LAND SURVEYOR, TO ALTER AN ITEM IN ANY WAY. IF AN ITEM BEARING THE STAMP OF A LICENSED PROFESSIONAL IS ALTERED, THE ALTERING ENGINEER, ARCHITECT, LANDSCAPE ARCHITECT, OR LAND SURVEYOR SHALL STAMP THE DOCUMENT AND INCLUDE THE NOTATION "ALTERED BY" FOLLOWED BY THEIR SIGNATURE, THE DATE OF SUCH ALTERATION, AND A SPECIFIC DESCRIPTION OF THE ALTERATION.							PARSONS			Department of Transportation

FILE NAME = c:\pwworking\hydot\p0030432\p00140571\p350204_cpt_6A.erw.dtl-sw1-10.dgn
DATE/TIME = 3/24/2026
USER = p0030432

DESIGN SUPERVISOR K.S. CHAU

JOB MANAGER C. LAMA


DESIGN J.P. O'LOUGHLIN

CHECK X. WANG


DRAFTING J.P. O'LOUGHLIN

CHECK X. WANG


PROJECT MANAGER C. LAMA

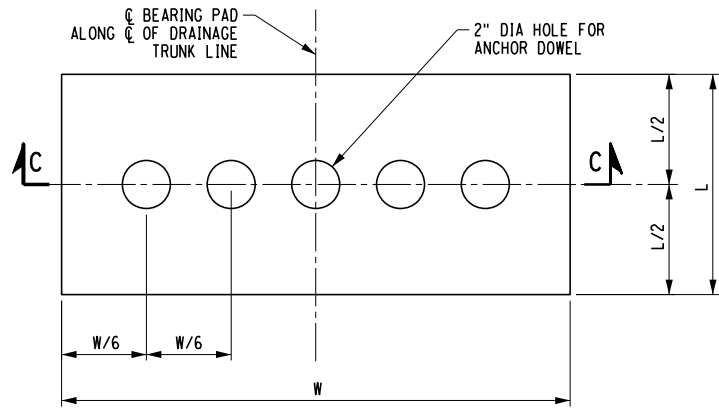

PLAN
PLAIN ELASTOMERIC BEARING (TYPE E.P.)

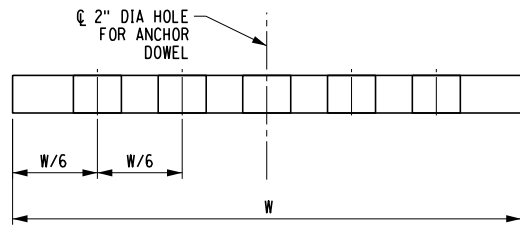

SECTION C-C

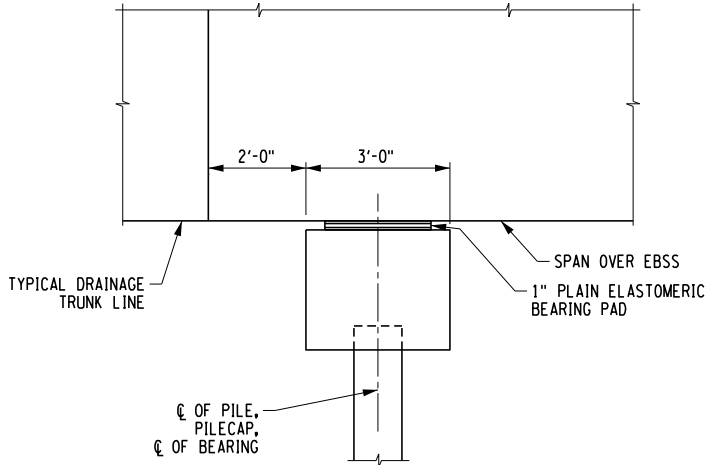

TYPICAL PIER ELEVATION


CROSSING 1 PLAIN ELASTOMERIC BEARING (TYPE E.P.) TABLE														
LOCATION	FIX/ EXP	ITEM NO	QUANTITY REQUIRED	D.L. + EV (kips)	WA (kips)	TOTAL DESGN (REACTION (kips)	SHAPE FACTOR	ELASTOMER LAYER			H	COMP. AREA (SQ in)	SHEAR AREA (SQ in)	ANCHOR DOWEL DIAMETER
								H	L	W				
PIER 1	EXP	565.1821	1	417	73	490	12.5	1	30	150	1	4500	4500	1
PIER 2	EXP	565.1821	1	417	73	490	12.5	1	30	150	1	4500	4500	1

CROSSING 2 PLAIN ELASTOMERIC BEARING (TYPE E.P.) TABLE														
LOCATION	FIX/ EXP	ITEM NO	QUANTITY REQUIRED	D.L. + EV (kips)	WA (kips)	TOTAL DESGN (REACTION (kips)	SHAPE FACTOR	ELASTOMER LAYER			H	COMP. AREA (SQ in)	SHEAR AREA (SQ in)	ANCHOR DOWEL DIAMETER
								H	L	W				
PIER 1	EXP	565.1821	1	230	30	260	11.5	1	30	100	1	3000	3000	1
PIER 2	EXP	565.1821	1	230	30	260	11.5	1	30	100	1	3000	3000	1


BEARING NOTES:
THE BEARINGS SHALL MEET REQUIREMENTS OF N.Y.S. STANDARD SPECIFICATION SECTION 565 UNLESS OTHERWISE NOTE.)

ELASTOMETER SHALL BE 60 DUROMETER HARDNESS ON THE SHORE A SCALE.


CONCRETE SURFACES UNDER THE BEARING SHALL CONFORM TO SUBSECTION 565-3.02 "CONCRETE BEARING SURFACE PREPARATION" OF THE N.Y.S. STANDARD SPECIFICATION, CONSTRUCTION AND MATERIALS.

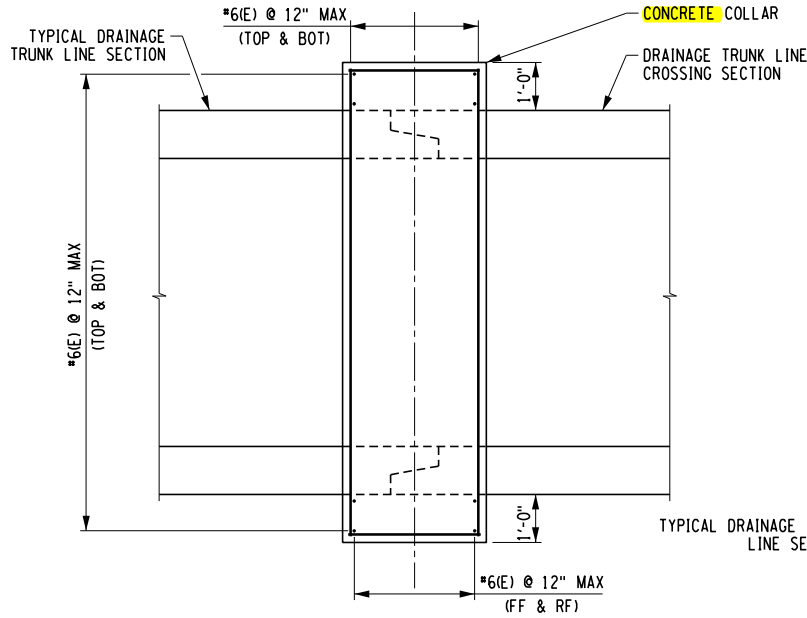

DRAINAGE TRUNK LINE COLLAR - PLAN
NTS

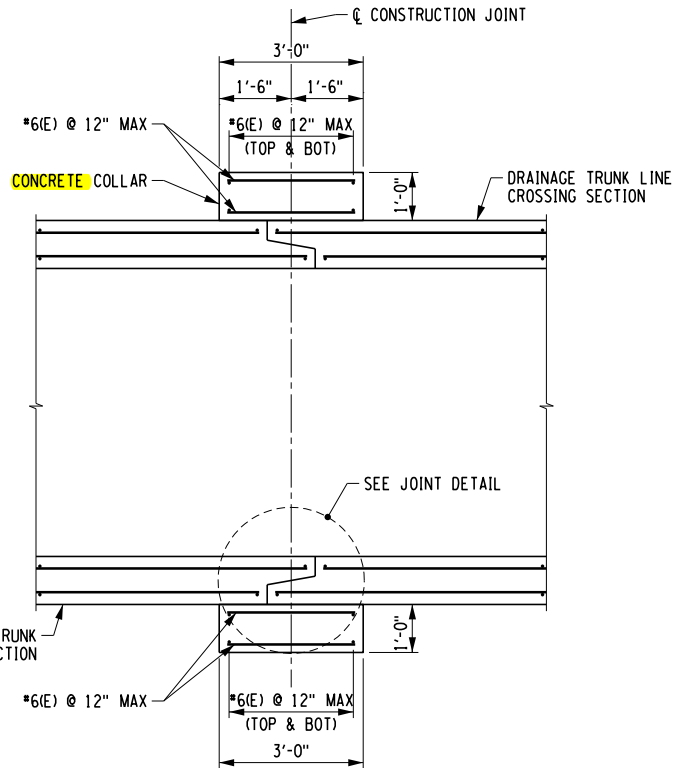

DRAINAGE TRUNK LINE COLLAR - SECTION
NTS

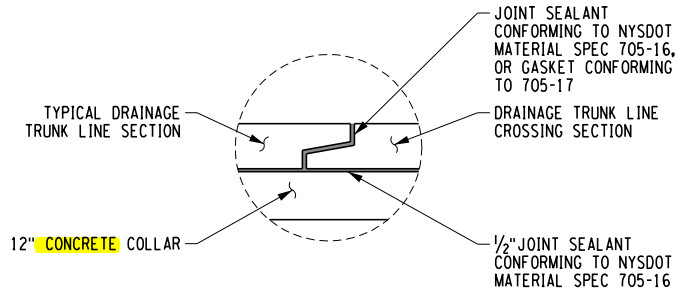

DRAINAGE TRUNK LINE JOINT - DETAIL
NTS

AFFIX SEAL:
ON: 03/26/2026

ALTERED BY:
ON:

AS-BUILT REVISIONS DESCRIPTION OF ALTERATIONS:	I-81 VIADUCT (COMMUNITY GRID) - CONTRACT 6A	PIN 3502.04		BRIDGES	CULVERTS	ALL DIMENSIONS IN FT UNLESS OTHERWISE NOTED	CONTRACT NUMBER	
	CITY OF SYRACUSE						D265702	
	WATER STREET, SALINA STREET AND HERALD PLACE						TRUNK LINE OVER EBSS DETAILS SHEET 3 OF 4	
	COUNTY: ONONDAGA REGION: 3							
IT IS A VIOLATION OF LAW FOR ANY PERSON, UNLESS THEY ARE ACTING UNDER THE DIRECTION OF A LICENSED PROFESSIONAL ENGINEER, ARCHITECT, LANDSCAPE ARCHITECT, OR LAND SURVEYOR, TO ALTER AN ITEM IN ANY WAY. IF AN ITEM BEARING THE STAMP OF A LICENSED PROFESSIONAL IS ALTERED, THE ALTERING ENGINEER, ARCHITECT, LANDSCAPE ARCHITECT, OR LAND SURVEYOR SHALL STAMP THE DOCUMENT AND INCLUDE THE NOTATION "ALTERED BY" FOLLOWED BY THEIR SIGNATURE, THE DATE OF SUCH ALTERATION, AND A SPECIFIC DESCRIPTION OF THE ALTERATION.						PARSONS	 NEW YORK STATE Department of Transportation	

FILE NAME = c:\pwworking\hydot\p0030432\040140571\0350204_cpt_6A_erw.dgn
DATE/TIME = 3/24/2026
USER = p0030432

DESIGN SUPERVISOR K.S. CHAU

JOB MANAGER C. LAMA


DESIGN J.P. O'LOUGHLIN

CHECK X. WANG


DRAFTING J.P. O'LOUGHLIN

CHECK X. WANG


PROJECT MANAGER C. LAMA

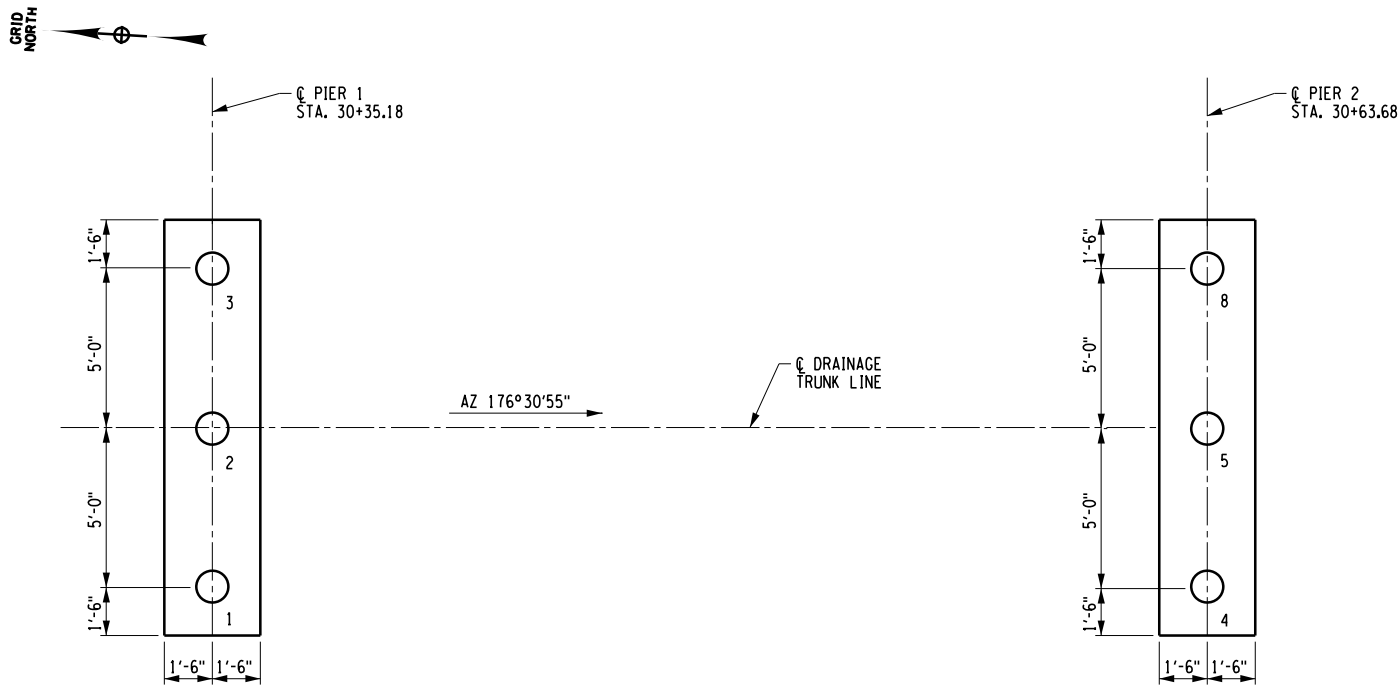


DRAINAGE TRUNK LINE EBSS CROSSING 1 - PILE LAYOUT PLAN

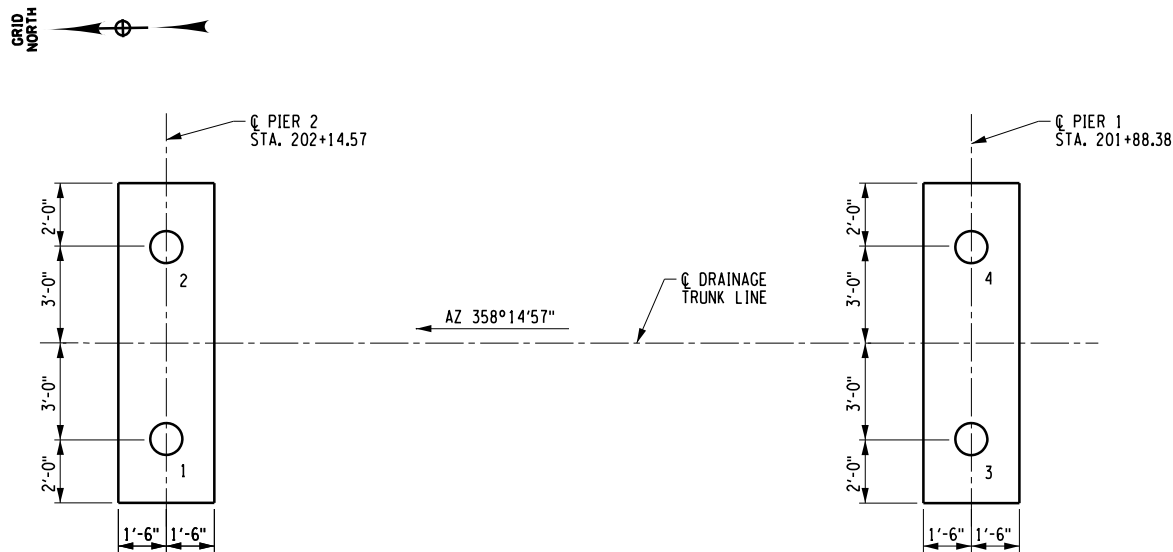


DRAINAGE TRUNK LINE EBSS CROSSING 2 - PILE LAYOUT PLAN

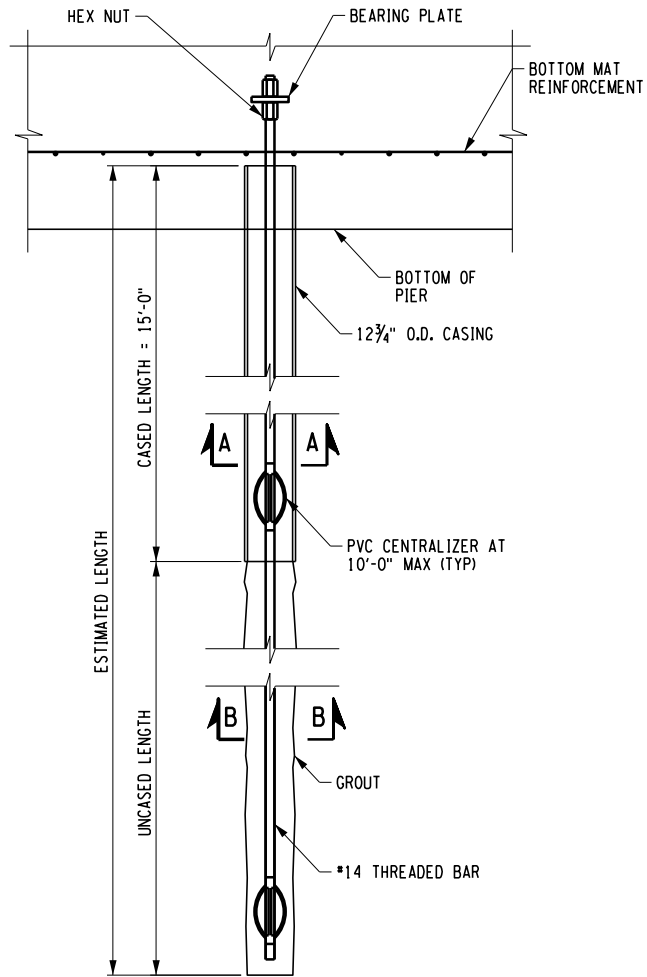

TYPICAL MICROPILE ELEVATION
SCALE: N.T.S.

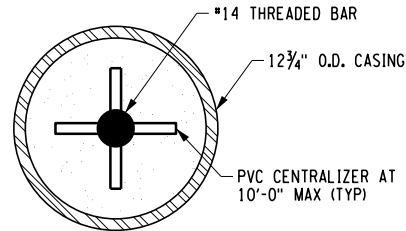

MICROPILE SECTION A-A
SCALE: N.T.S.

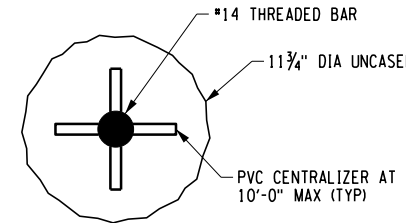

MICROPILE SECTION B-B
SCALE: N.T.S.

MICROPILE NOTES:

1. TYPE A MICROPILES AT CROSSING 1 WILL SUPPORT A MAXIMUM STRENGTH LIMIT STATE OF 212 KIPS PER PILE. INSTALL THESE TO ACHIEVE A NOMINAL RESISTANCE OF 424 KIPS PER PILE. THE MAXIMUM SERVICE LIMIT STATE AXIAL LOAD APPLIED TO THE TYPE A MICROPILES AT CROSSING 1 IS 163 KIPS PER PILE.
2. TYPE B MICROPILES AT CROSSING 2 WILL SUPPORT A MAXIMUM STRENGTH LIMIT STATE OF 171 KIPS PER PILE. INSTALL THESE PILES TO ACHIEVE A NOMINAL RESISTANCE OF 342 KIPS PER PILE. THE MAXIMUM SERVICE LIMIT STATE AXIAL LOAD APPLIED TO THE TYPE A MICROPILES AT CROSSING 2 IS 130 KIPS PER PILE.
3. PERFORM 1 STATIC PILE LOAD TEST, ITEM 551.35 ON A NON-PRODUCTION PILE INSTALLED IN THE VICINITY OF EACH CROSSING. PROVIDE A BOND BREAKER ABOVE ELEVATION 364.50 FOR CROSSING 1, AND 364.00 FOR CROSSING 2. PERFORM THIS TEST PRIOR TO THE INSTALLATION OF ANY PRODUCTION PILES.
4. COST OF TEST PILES INCLUDED UNDER STATIC LOAD TEST, ITEM 551.35.
5. DESIGN MICROPILES SO THAT THE GROSS VERTICAL TOP MOVEMENT OF THE PILE DURING LOAD TESTING DOES NOT EXCEED 1 INCH AT THE SERVICE LIMIT STATE OF AXIAL LOADS.

AFFIX SEAL:
ON: 03/26/2026

ALTERED BY:
ON:



AS-BUILT REVISIONS
DESCRIPTION OF ALTERATIONS:

I-81 VIADUCT (COMMUNITY GRID) - CONTRACT 6A

CITY OF SYRACUSE

WATER STREET, SALINA STREET AND HERALD PLACE

COUNTY: ONONDAGA

REGION: 3

PIN 3502.04

BRIDGES

CULVERTS

ALL DIMENSIONS IN FT UNLESS OTHERWISE NOTED

CONTRACT NUMBER

D265702

TRUNK LINE OVER EBSS

DETAILS

SHEET 4 OF 4

DRAWING NO.

SW1-11

SHEET NO.

266

IT IS A VIOLATION OF LAW FOR ANY PERSON, UNLESS THEY ARE ACTING UNDER THE DIRECTION OF A LICENSED PROFESSIONAL ENGINEER, ARCHITECT, LANDSCAPE ARCHITECT, OR LAND SURVEYOR, TO ALTER AN ITEM IN ANY WAY. IF AN ITEM BEARING THE STAMP OF A LICENSED PROFESSIONAL IS ALTERED, THE ALTERING ENGINEER, ARCHITECT, LANDSCAPE ARCHITECT, OR LAND SURVEYOR SHALL STAMP THE DOCUMENT AND INCLUDE THE NOTATION "ALTERED BY" FOLLOWED BY THEIR SIGNATURE, THE DATE OF SUCH ALTERATION, AND A SPECIFIC DESCRIPTION OF THE ALTERATION.

PARSONS



Department of
Transportation